



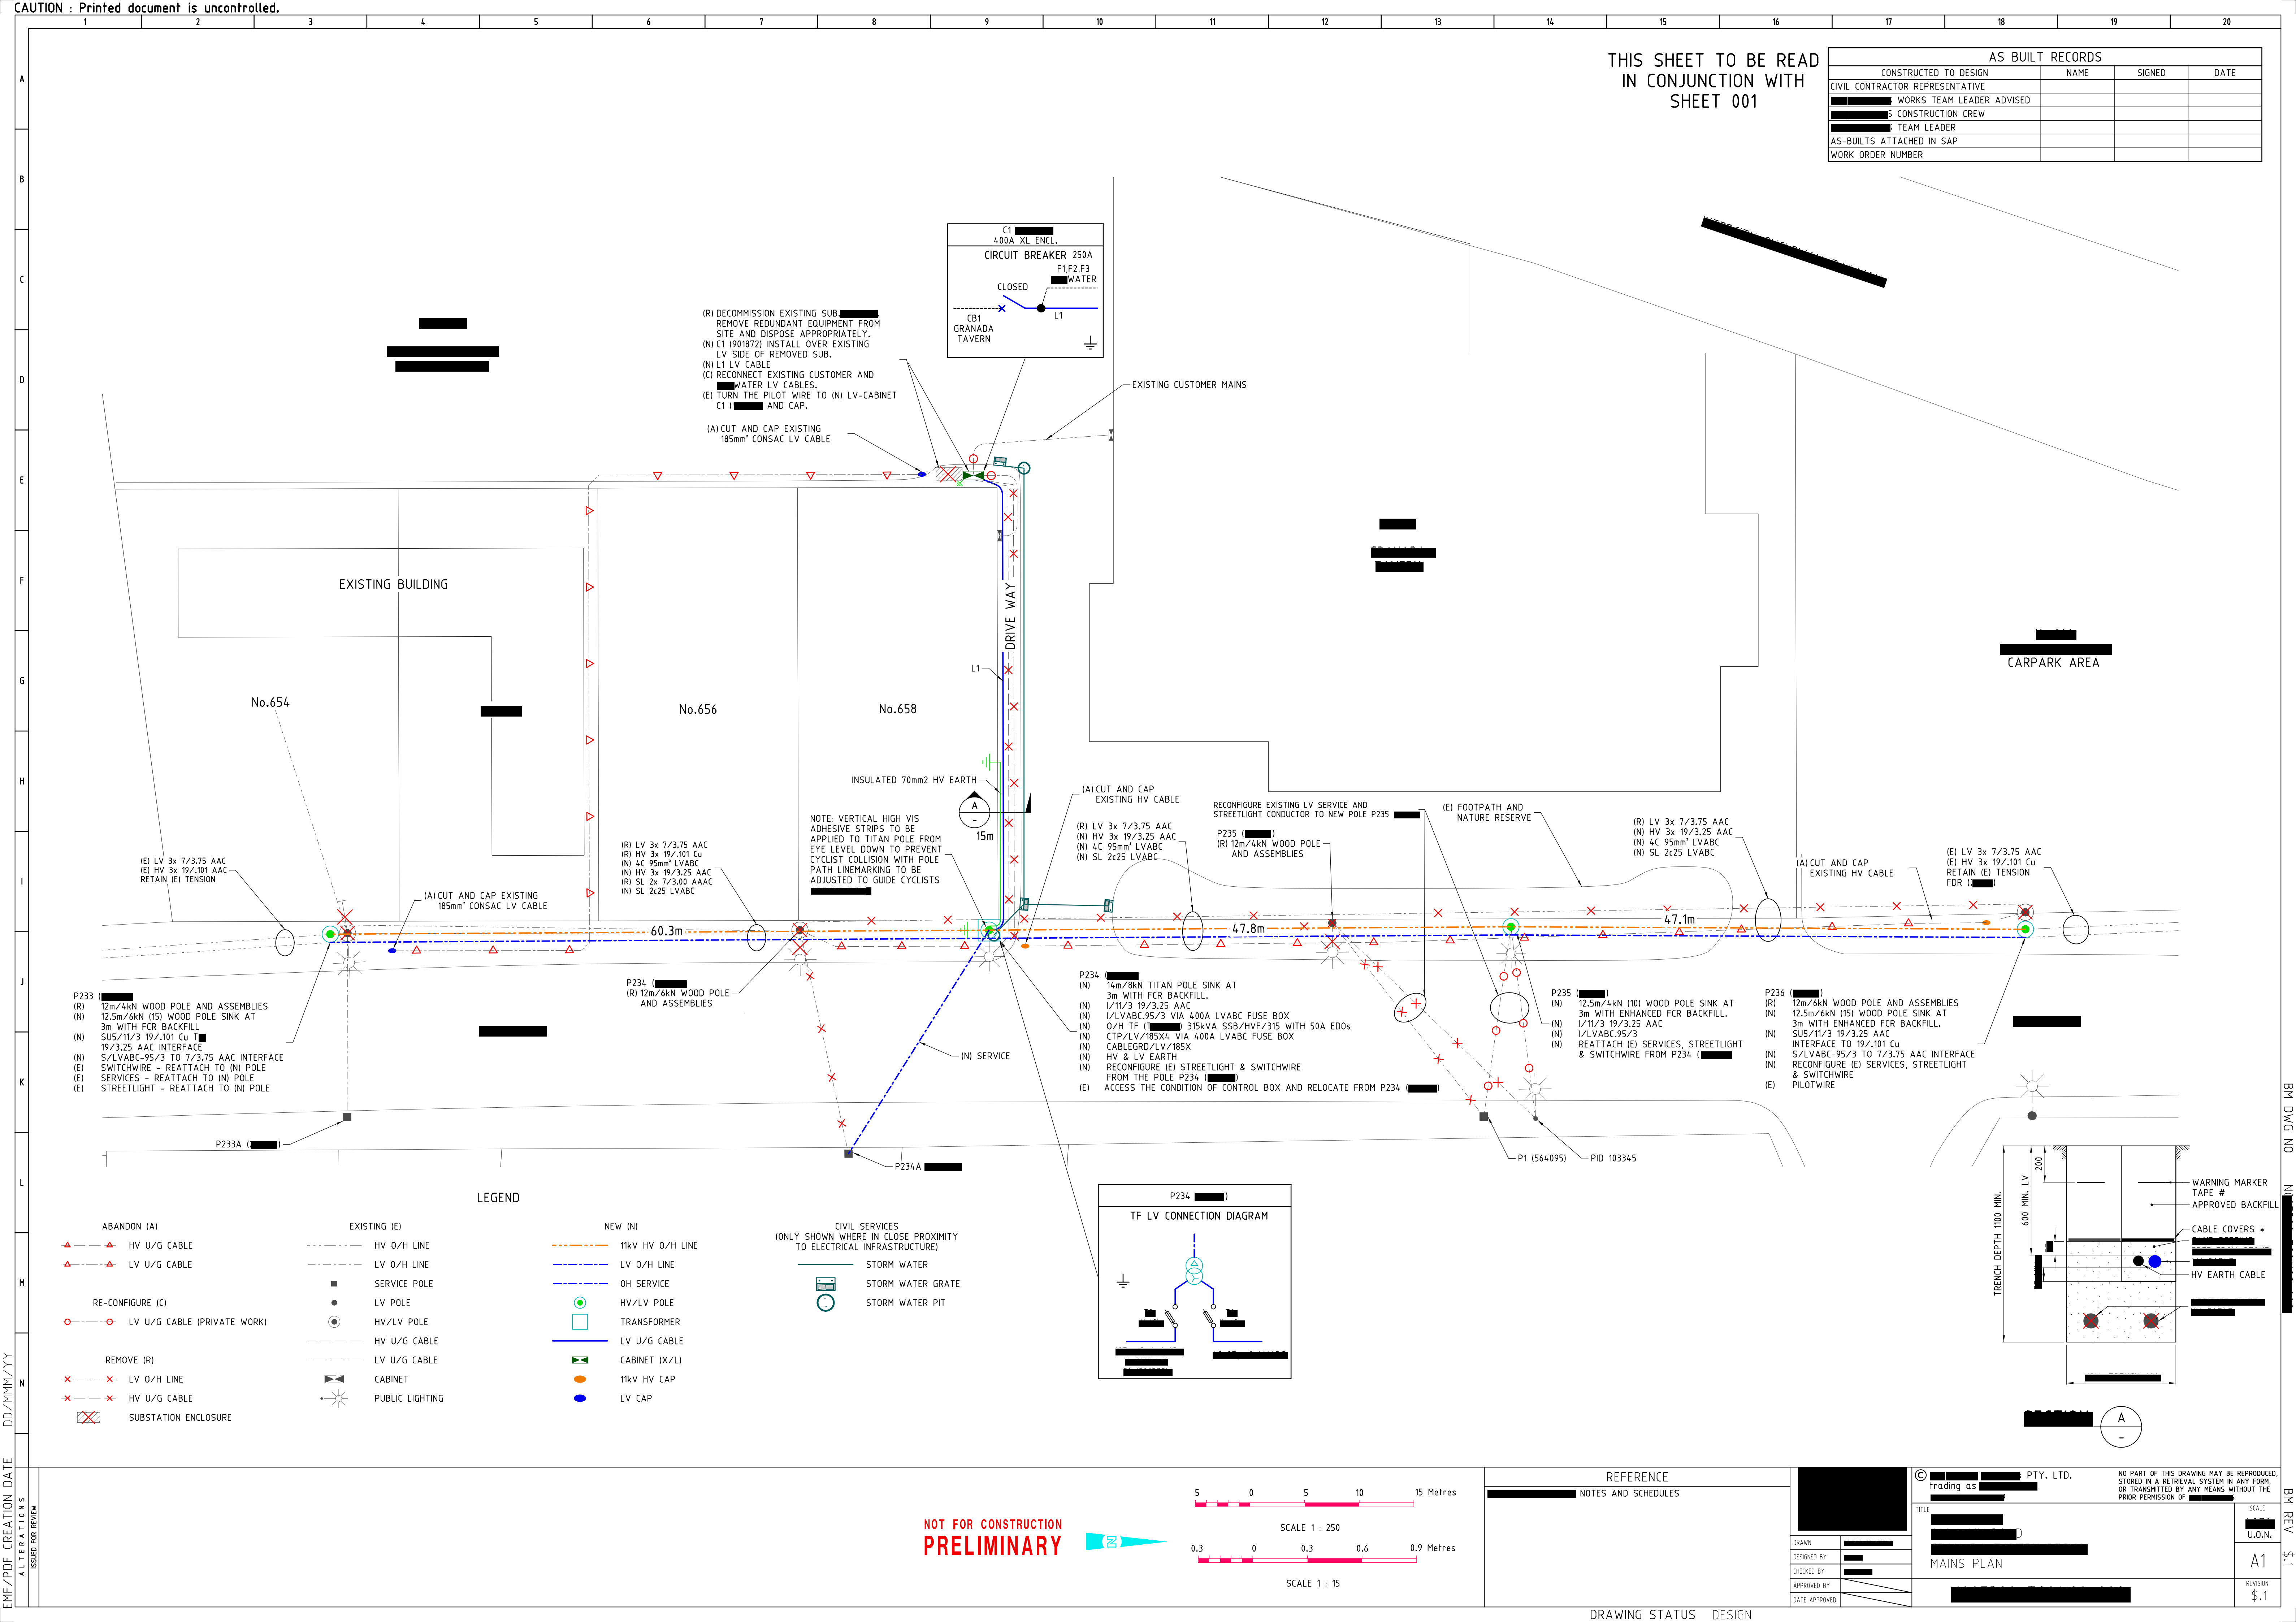

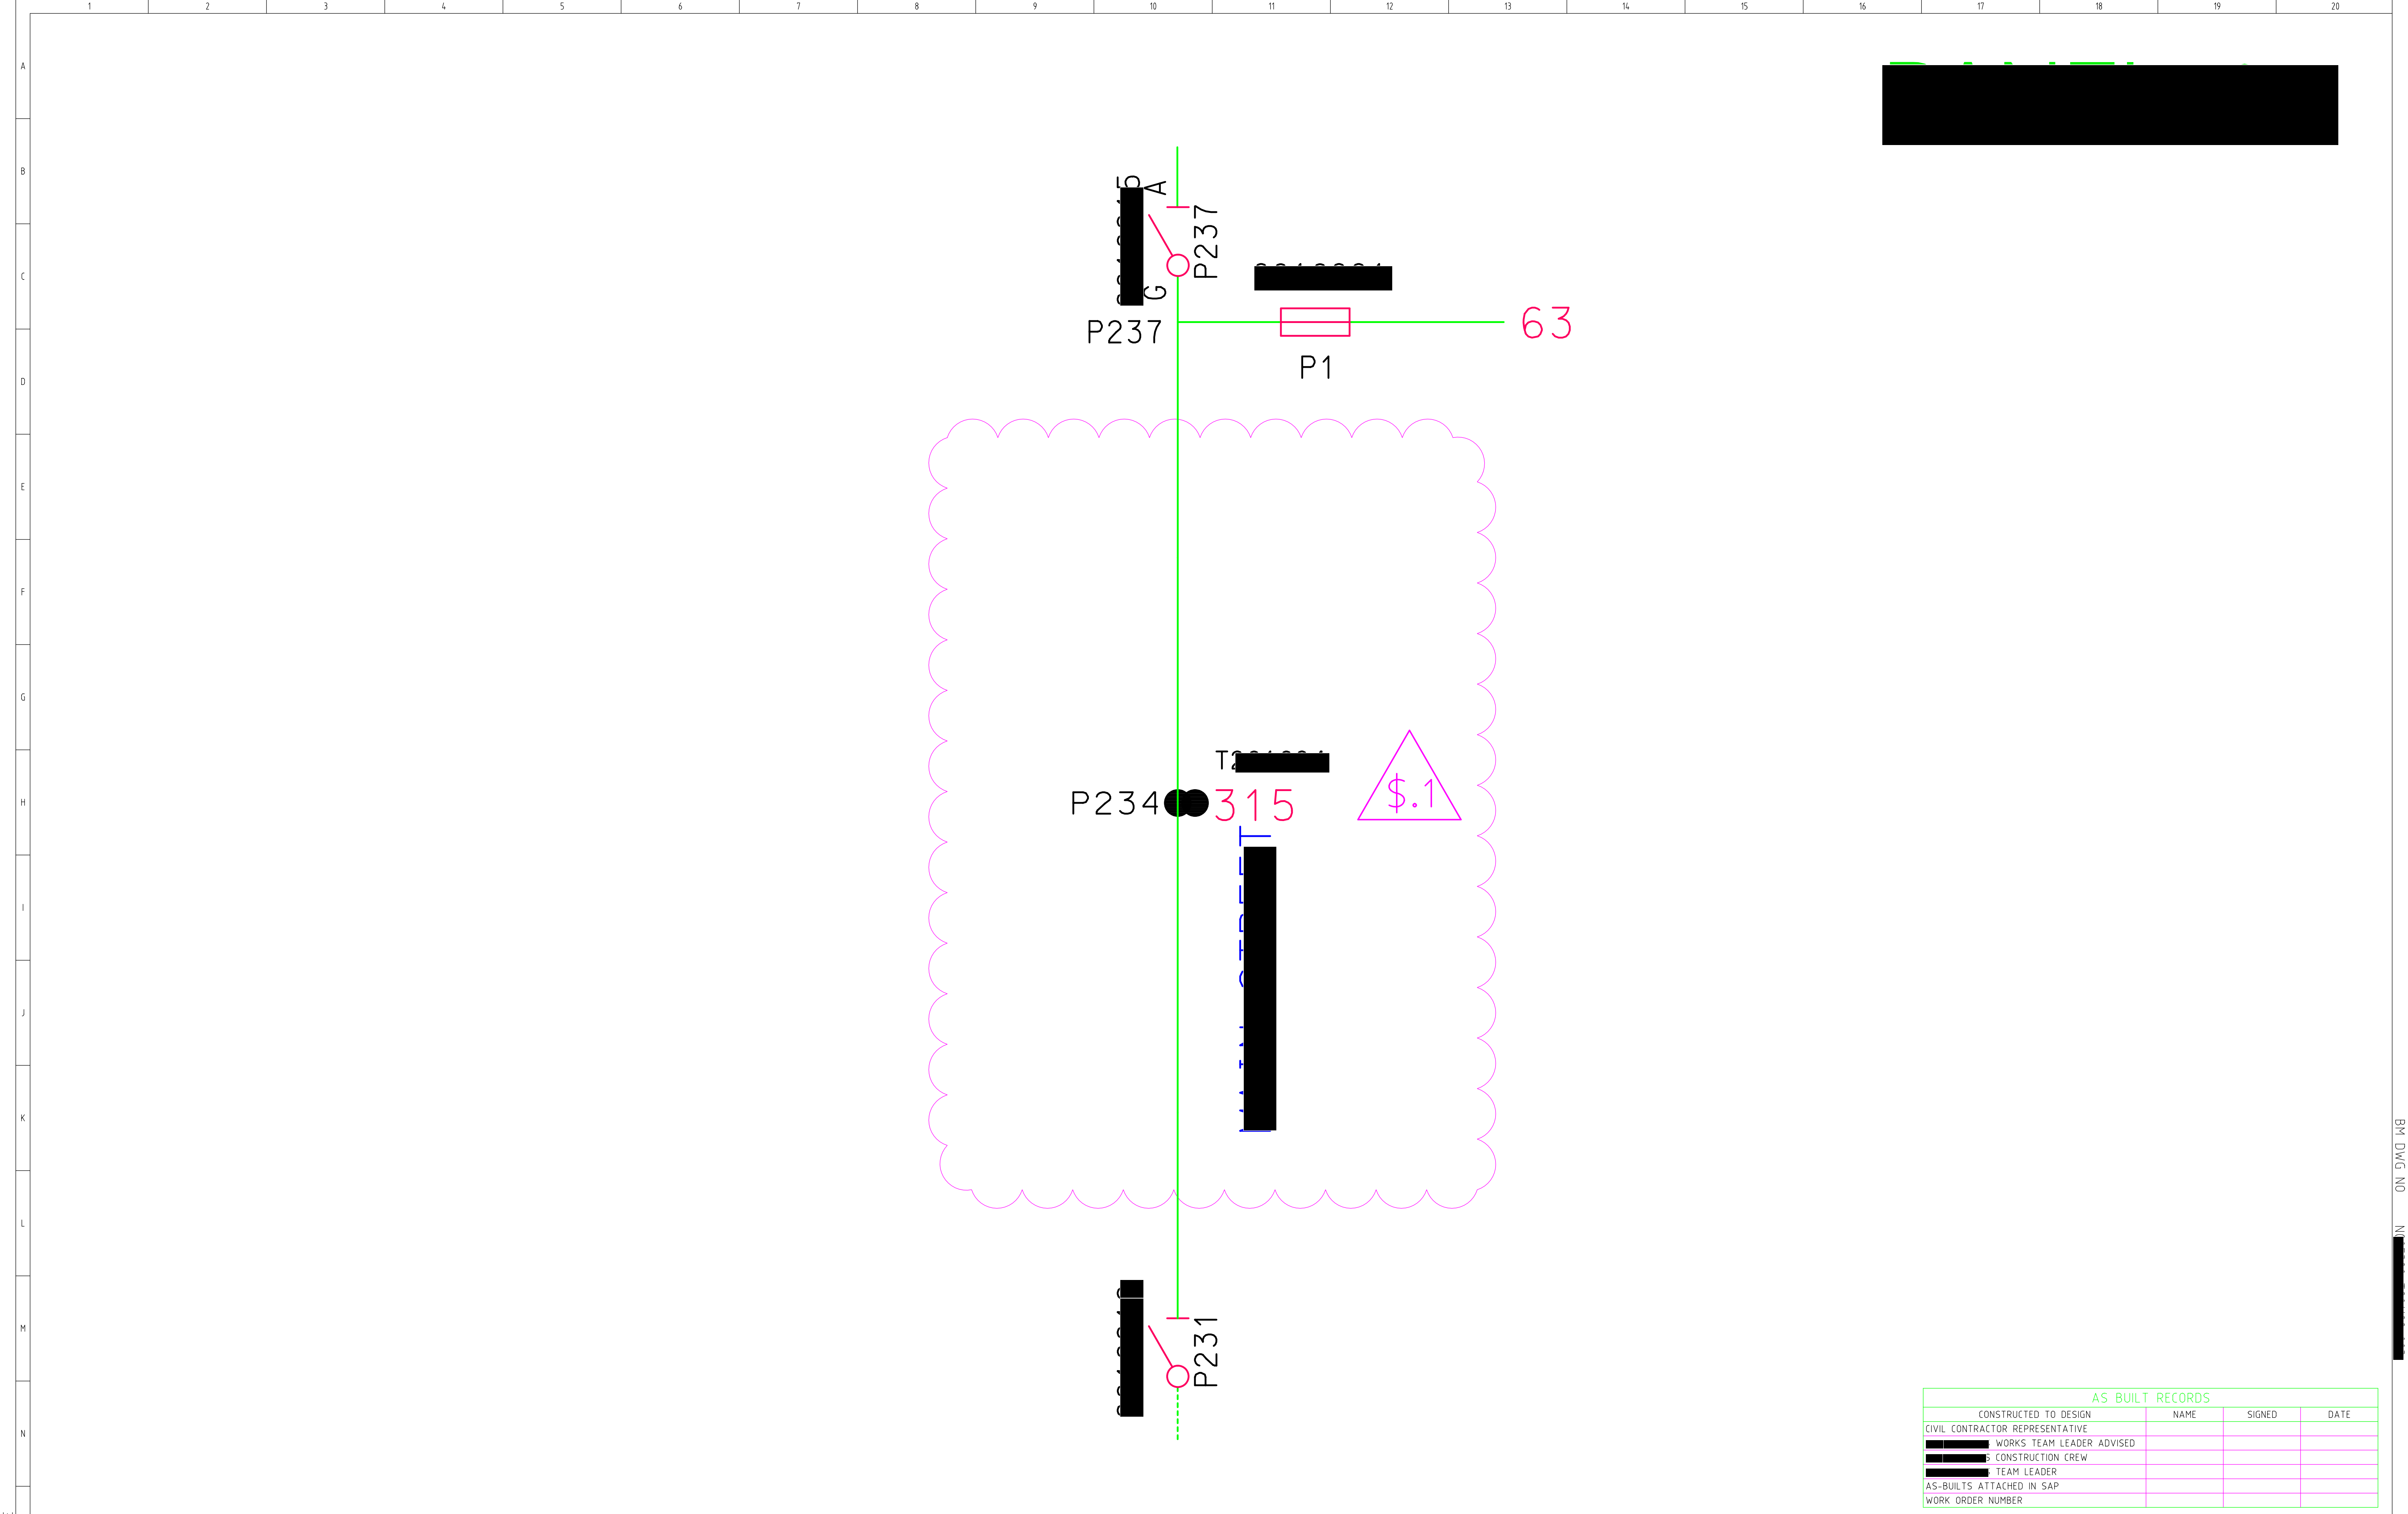

ENF/PDF CREATION DATE
ALTERATIONS
WP

NOT FOR CONSTRUCTION
PRELIMINARY

REFERENCE	
MAINS PLAN	

DRAWN		[Redacted Signature]	© [Redacted] PTY. LTD. Trading as [Redacted] ABN: 24 167 357 299	NO PART OF THIS DRAWING MAY BE REPRODUCED, STORED IN A RETRIEVAL SYSTEM IN ANY FORM, OR TRANSMITTED BY ANY MEANS WITHOUT THE PRIOR PERMISSION OF [Redacted]	SCALE A1				
DESIGNED BY									
CHECKED BY									
APPROVED BY									
DATE APPROVED		[Redacted Signature]		REVISION					

BM DWG NO. N
BM REV. \$1